Ərizə: 1119075333

Ödəyən: Azərbaycan Respublikası Təhsil Nazirliyi,
Bakı şəhəri üzrə təhsil İdarəsi

AR ƏMDKY DƏDRX
1 saylı Bakı Ərazi İdarəsi
VÖEN: 1500067091
Bank: Kapital Bankın "Nərimanov" filialı
H/h: AZ 53 AİİB 33040019443901777109
M/h: AZ 37NABZ013 501 00000000001944
Kod: 200093
VOEN: 9900003611
S.W.I.F.T.BIK- AIIBAZ 2X

VÖEN : 1400617761

H E S A B № 273

26 avqust 2019-cu il

Verilmiş hesab iyirmi bank günü müddətində etibarlıdır.Idarənin bank hesabına çatmamış məbləğlərə bu müddətdən sonra baxılır və yeni qiymətlər təyin edilir.

	ADI	Ölçü vah	Miqdar	Qiymət	Məbləği
1	Azərbaycan Respublikası Təhsil Nazirliyi, Bakı şəhəri üzrə Təhsil İdarəsinin tabeliyində olan və Bakı şəhəri, Binəqədi rayonu, M.Ə.Rəsulzadə qəsəbəsi , Azadlıq prospekti , 193 ünvanda yerləşən 99 nömrəli tam orta məktəbə məxsus qeyri-yaşayış binasına və torpaq sahəsinə texniki pasportun hazırlanması üçün ödənilmiş məbləğ				
	1.Daşınmaz əmlakın inventarlaşdırılması üçün ödəniş	kv.metr	7042.7		2248.14
	2.Torpaq sahəsinin inventarlaşdırılması üçün xidmət haqqı	ha	0.56133		306.28
	Cəmi:				2554.42
	ƏDV 18% +				459.80
2	3.Texniki pasport üçün dövlət rüsumu	ədəd	1	50.00	50.00
	Yekunu:				**3064.22**

Ödəniləsi məbləğ: İki min altmış dörd manat -22 qəpik.

DƏDRX-nin 1 saylı Bakı Ərazi Idarəsinin rəisvəzifəsini icra edən F.T.Bağırov

Maliyyə şöbəsinin müdiri M.Ə.Talıbov

Azərbaycan Respublikası Əmlak Məsələləri Dövlət Komitəsi sədrinin 43 nömrəli 21 aprel 2010-cu il tarixli əmri ilə təsdiq edilmişdir

Azərbaycan Respublikası
Əmlak Məsələləri Dövlət Komitəsinin
yanında
Daşınmaz Əmlakın Dövlət Reyestri Xidməti

1 saylı Bakı Ərazi İdarəsi

Texniki Pasport

Qeyri-yaşayış binası

Adı: Qeyri yaşayış binası – 99 №-li tam orta məktəb

Ünvan: Bakı şəhəri, Binəqədi rayonu, M.Ə.Rəsulzadə qəsəbəsi, Azadlıq prospekti, 193

Balans saxlayıcı: Azərbaycan Respublikası Təhsil Nazirliyi, Bakı Şəhəri üzrə Təhsil İdarəsi

İcarəçi və ya istifadəçi:

Hüquq subyekti:

İnventar nömrəsi: 04/6688 11.09.2019

Reyestr nömrəsi: 001011007004-06101

Pasport 21.08.2019 tarixdə olan vəziyyətə əsasən tərtib olunub

Baş mühəndis: **R.Babayev**

M.Y

(imza) (s.a.a)

Azərbaycan Respublikası
Əmlak Məsələləri Dövlət Komitəsinin yanında
Daşınmaz Əmlakın Dövlət Reyestri Xidmətinin
1 saylı Bakı Ərazi İdarəsi

DAŞINMAZ ƏMLAKIN
TEXNİKİ İNVENTORLAŞDIRILMASI
ŞÖBƏSİ
KORRENTƏ EDİLDİ

Axundova
(vəzifəsi, adının baş hərfi, soyadı) (imza)


« 11 » 09 2019 il

Azərbaycan Respublikası
Əmlak Məsələləri Dövlət Komitəsinin yanında
Daşınmaz Əmlakın Dövlət Reyestri Xidmətinin
1 saylı Bakı Ərazi İdarəsi


№ 04/6688

« 11 » 09 2019 il

ş plan
1:300

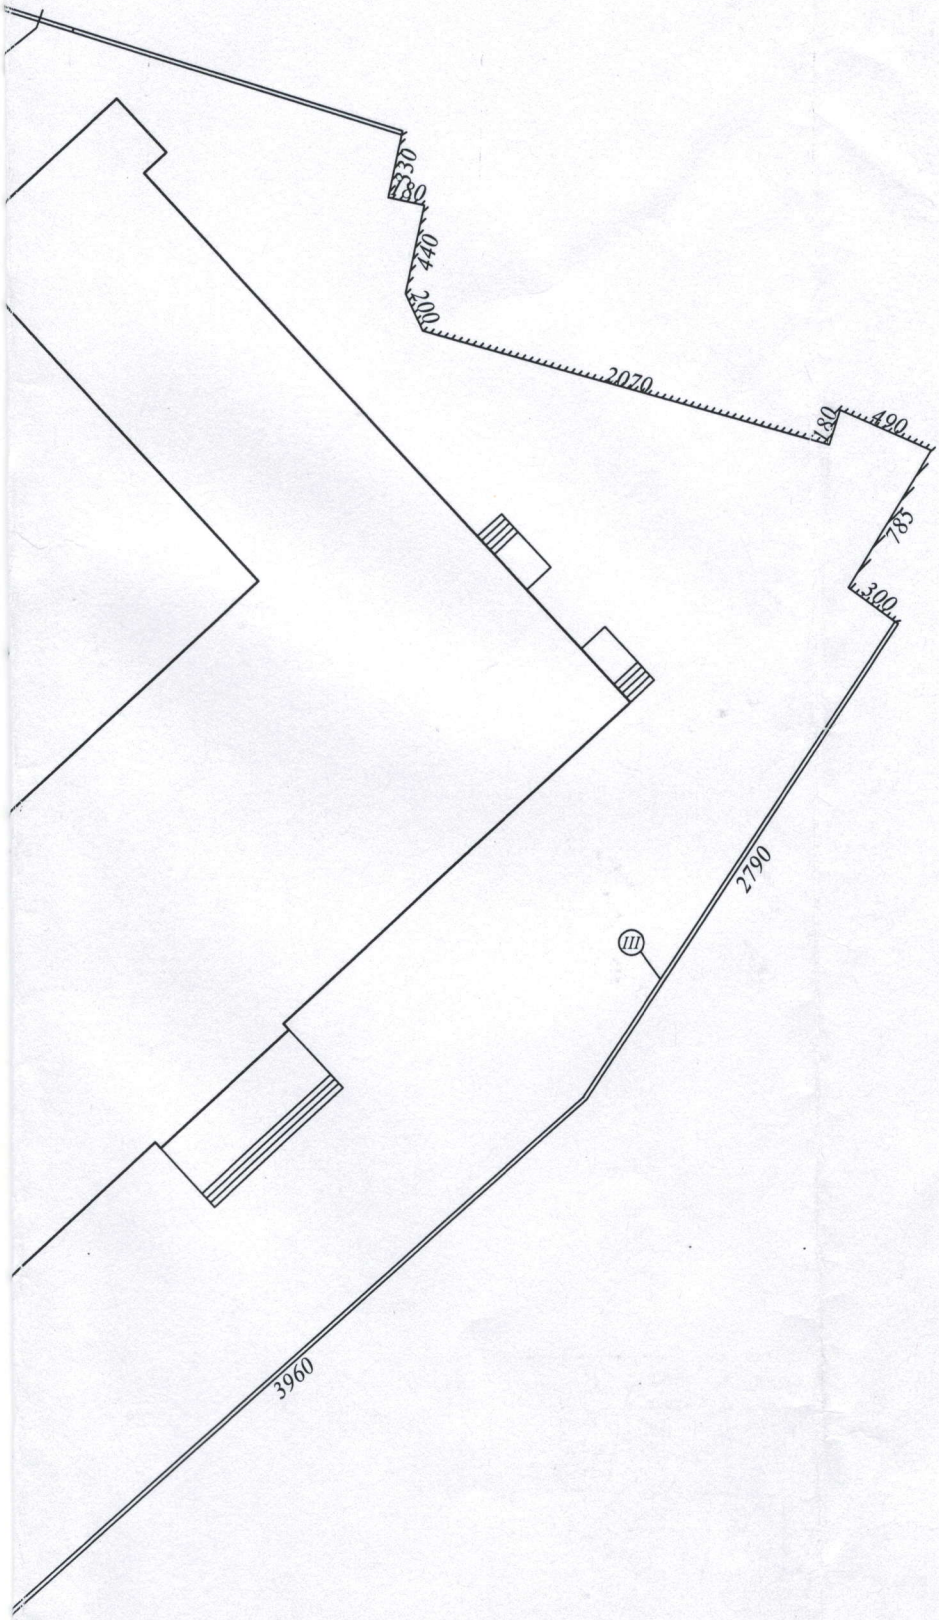


Şərti istinad planı

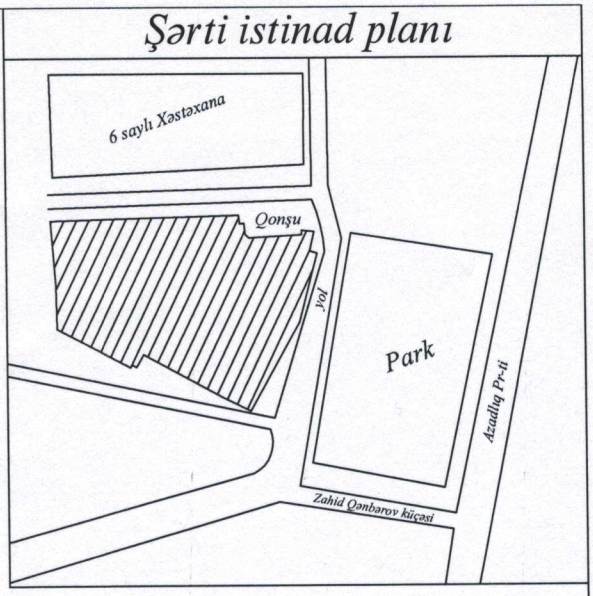

Azərbaycan Respublikası
Əmlak Məsələləri Dövlət Komitəsinin yanında
Daşınmaz Əmlakın Dövlət Reyestri Xidmətinin
1 saylı Bakı Ərazi İdarəsi
Daxilolma № 04/6688
« 11 » 09 2019 il


Ba
M

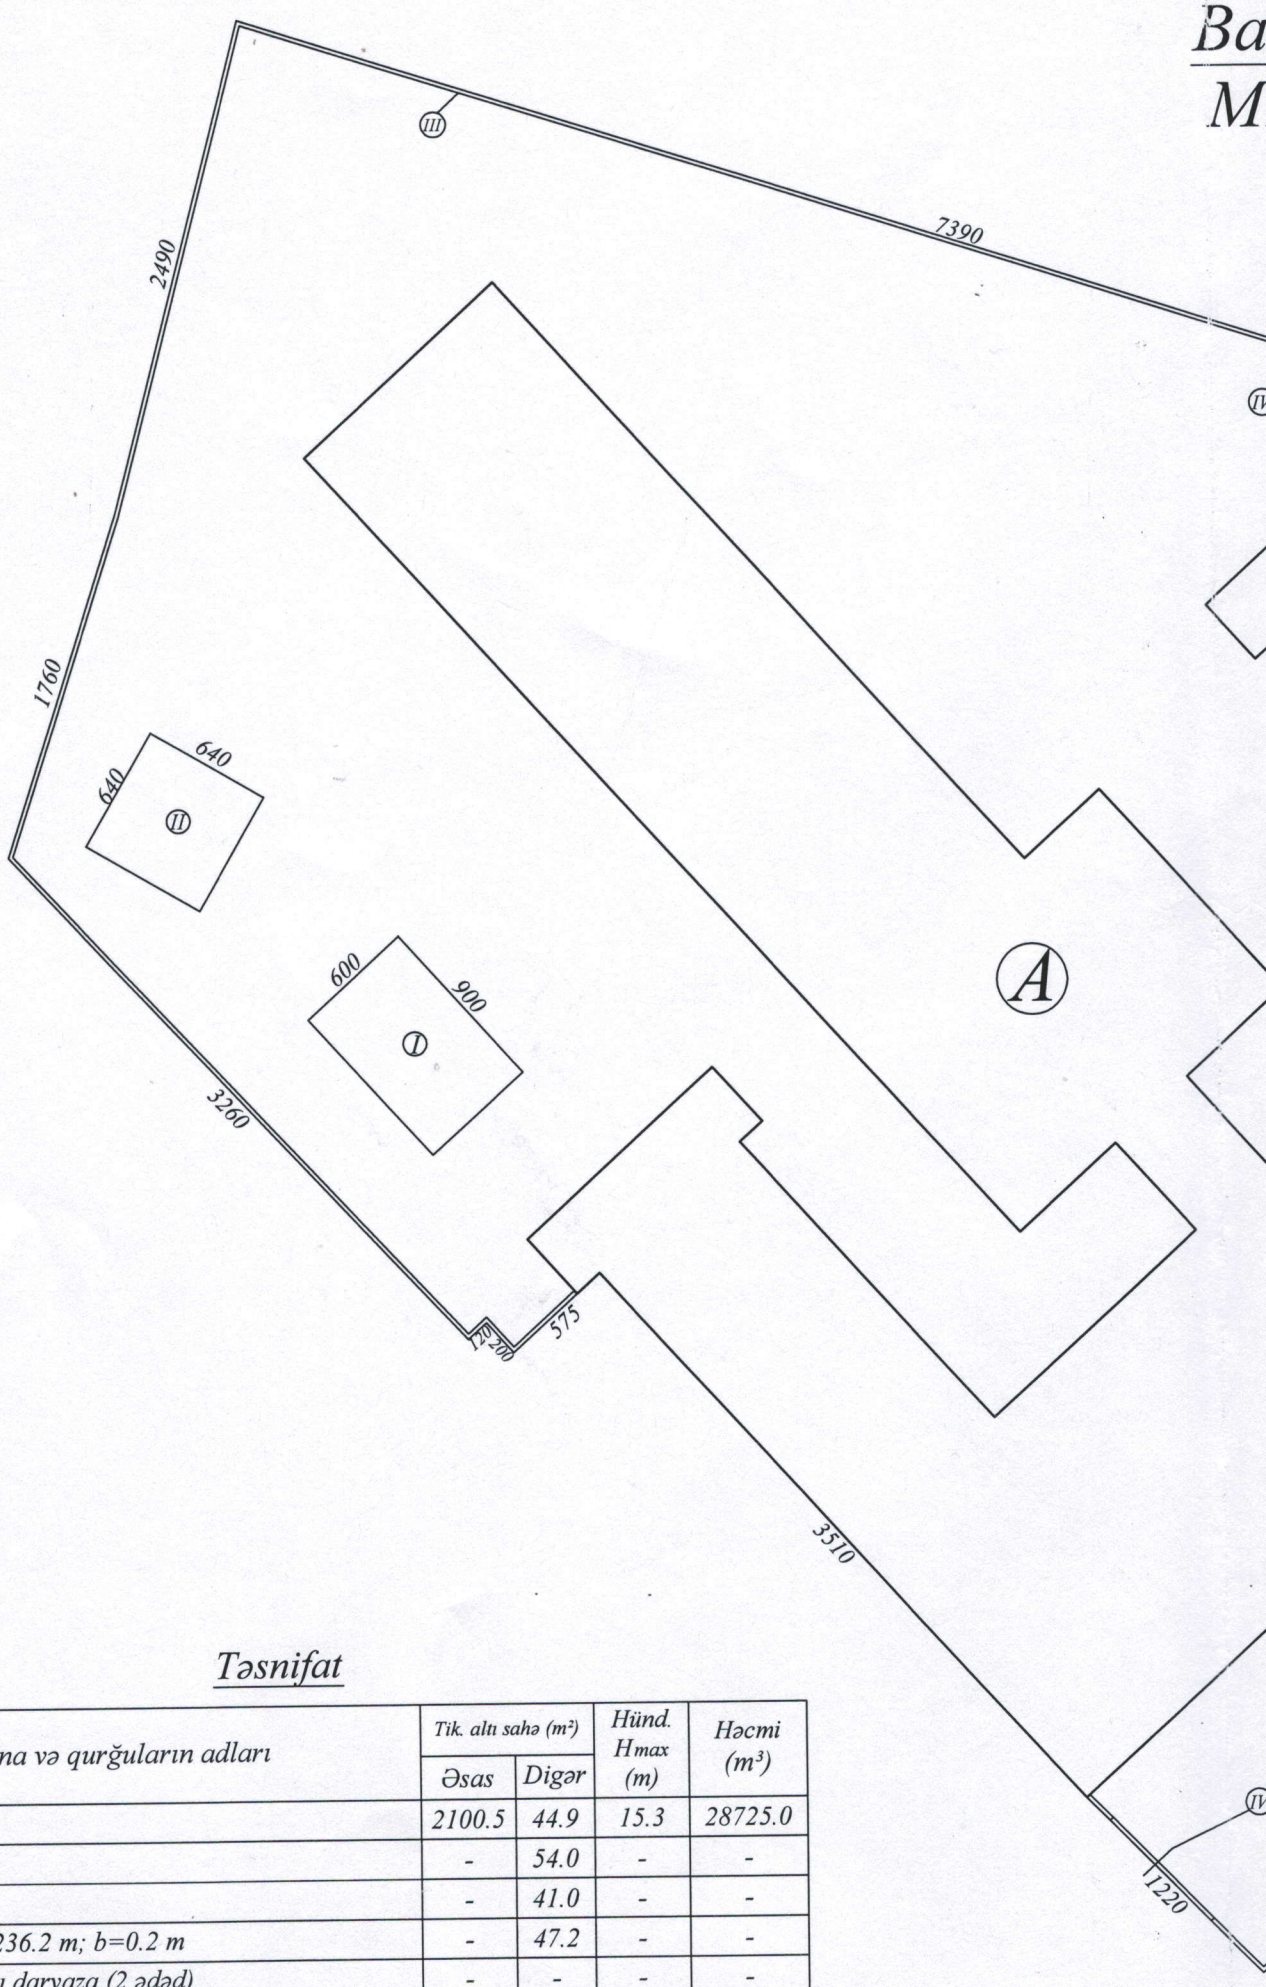

Təsnifat

Liter	Bina və qurğuların adları	Tik. altı sahə (m²)		Hünd. Hmax (m)	Həcmi (m³)
		Əsas	Digər		
A	Məktəb binası	2100.5	44.9	15.3	28725.0
I	Su anbarı	-	54.0	-	-
II	Nasosxana	-	41.0	-	-
III	Daş hasar: L=236.2 m; b=0.2 m	-	47.2	-	-
IV	Dəmir barmaqlı darvaza (2 ədəd)	-	-	-	-
Ümumi tikilialtı sahə:	**2287.6 m²**	**2100.5**	**187.1**	**-**	**-**
Açıq torpaq sahəsi:	**3325.7** m²				
Ümumi torpaq sahəsi:	5613.3 m²				

əmisi) M1:100
3384.0m³

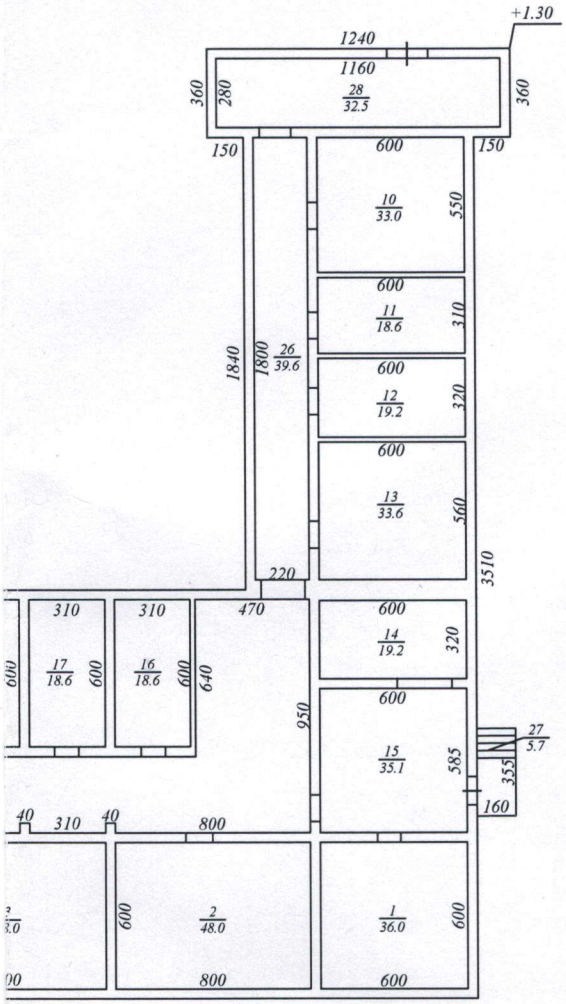

Təsnifat


S/N	OTAQLARIN TƏYİNATI	SAHƏLƏR (m²)		
		ƏSAS	KÖMƏK	DİGƏR
1-23	Zirzəmi	828.0	-	-
24-26	Dəhliz	-	251.1	-
27	Açıq pilləkan	-	-	5.7
28;29	Giriş	-	65.0	-
	Cəmi: 1144.1 m²	**828.0**	**316.1**	**5.7**

Azərbaycan Respublikası
Əmlak Məsələləri Dövlət Komitəsinin yanında
Daşınmaz Əmlakın Dövlət Reyestri Xidmətinin
1 saylı Bakı Ərazi İdarəsi
Daxilolma № 04/6688
« 11 » 09 2019 il

"A" Tikilisinin planı (4 mərtəbəli binanın zir

$h=2.20m$; $H=2.50m$; $S_{t.a.}=1353.7m^2$; V


$S_{t.a.digər}=5.7m^2$

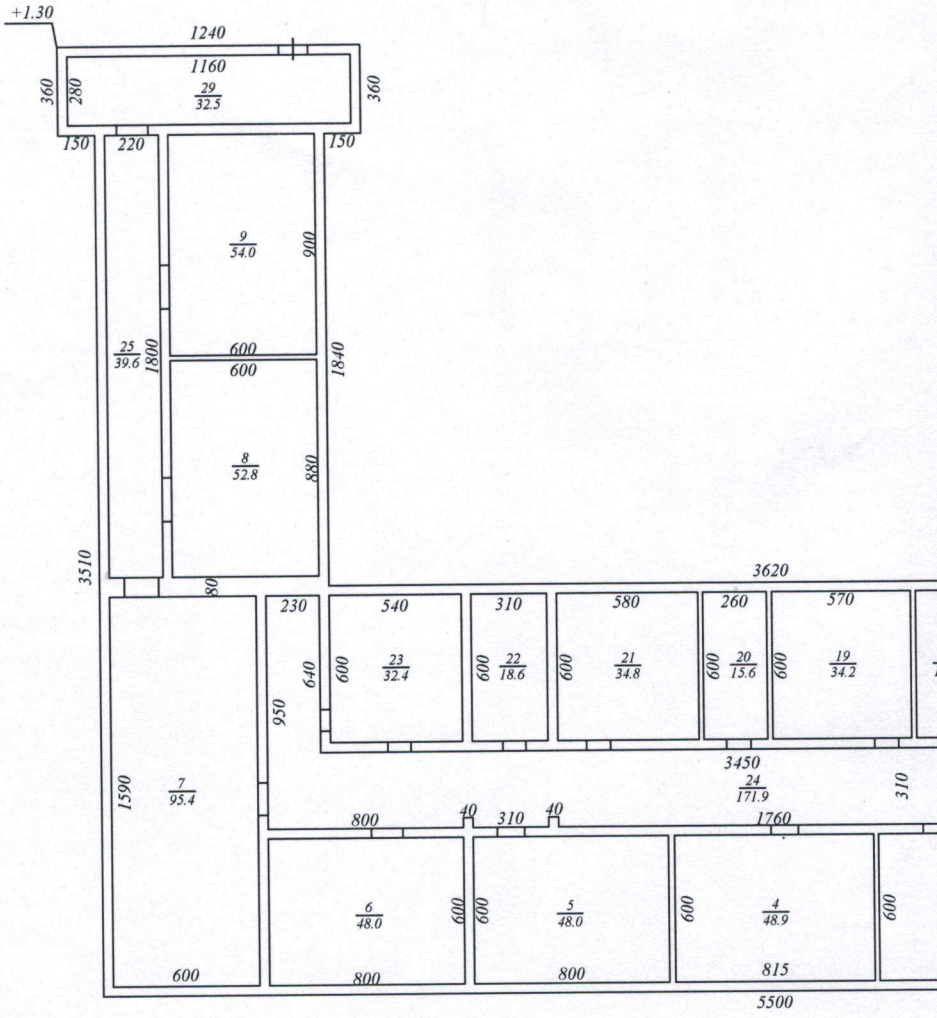

Qeyd: 1)Zirzəmi sahəsi su ilə dolu olduğundan 1-ci mərtəbənin yük daşıyan divarları əsasından tərtib olund

l-ci mərtəbəsi) M1:100

.0m³

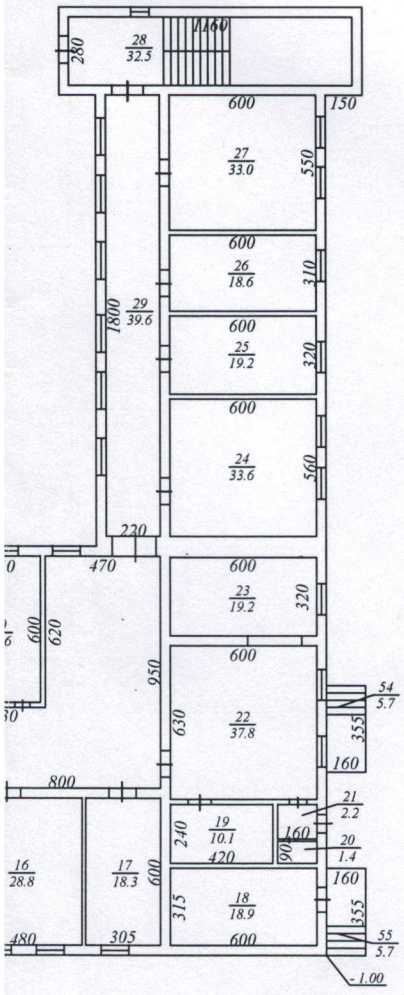

Təsnifat

h (m)	*H (m)*	*S/N*	*OTAQLARIN TƏYİNATI*	*SAHƏLƏR (m²)*		
				ƏSAS	*KÖMƏK*	*DİGƏR*
3.30	*3.60*	*1;6;7;10;11*	*Sinif otağı*	*234.8*	*-*	*-*
3.30	*3.60*	*2;3;4;29;34*	*Dəhliz*	*-*	*367.0*	*-*
3.30	*3.60*	*5;28;42*	*Pilləkan qəfəsi*	*-*	*81.8*	*-*
3.30	*3.60*	*8;9;12*	*İş otağı*	*40.5*	*-*	*-*
3.30	*3.60*	*13;14;30;50*	*İş otağı*	*60.6*	*-*	*-*
3.30	*3.60*	*15*	*Drektor otağı*	*30.0*	*-*	*-*
3.30	*3.60*	*16;24-27*	*Sinif otağı*	*133.2*	*-*	*-*
3.30	*3.60*	*17*	*Tibb otağı*	*-*	*18.3*	*-*
3.30	*3.60*	*18;19;39;51*	*Anbar*	*-*	*60.6*	*-*
3.30	*3.60*	*20;21;31;32*	*Sanitar qovşağı*	*-*	*20.4*	*-*
3.30	*3.60*	*22*	*Yemekxana*	*-*	*37.8*	*-*
3.30	*3.60*	*23*	*Mətbəx*	*-*	*19.2*	*-*
3.30	*3.60*	*33;36;41;45*	*Sinif otağı*	*141.0*		
3.30	*3.60*	*35;40;47;52*	*Dəhliz*		*156.5*	
3.30	*3.60*	*37;38;43;44*	*Sanitar qovşağı*		*31.4*	
3.30	*3.60*	*46*	*Sinif otağı*	*36.0*		
3.30	*3.60*	*48;49*	*Soyunub geyinmə otağı*	*-*	*38.8*	
6.00	*6.30*	*53*	*İdman zalı*	*-*	*279.1*	
-	*-*	*-*	*Açıq pilləkan*	*-*	*-*	*44.9*
			Cəmi: 1787.0 m²	***676.1***	***1110.9***	***44.9***

Azərbaycan Respublikası
Əmlak Məsələləri Dövlət Komitəsinin yanında
Daşınmaz Əmlakın Dövlət Reyestri Xidmətinin
1 saylı Bakı Ərazi İdarəsi


Daxilolma № 04/6688

« 11 » 09 2019 il

"A" Tikilisinin planı (4 mərtəbəli binanın


$S_{t.a.}$=2100.5m²; V=839

$S_{t.a.digər}$=44.9m²

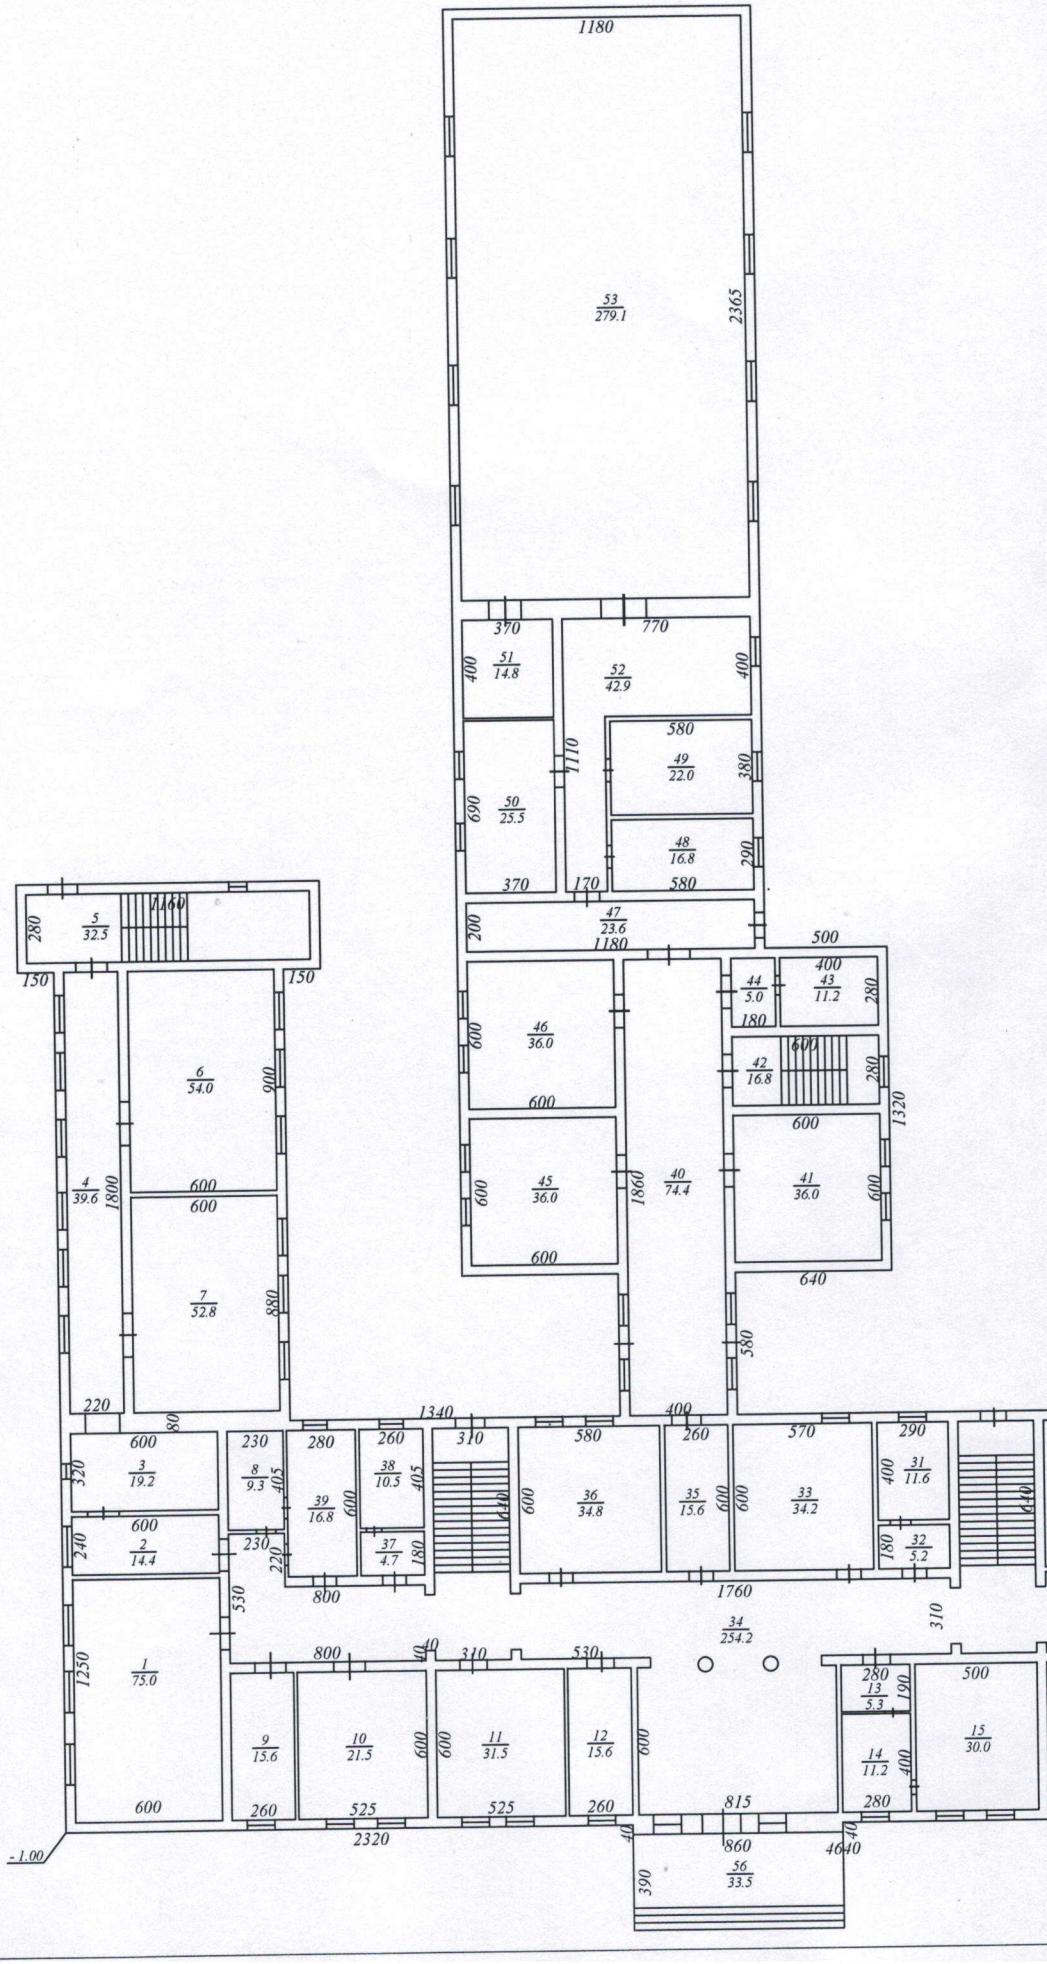

ının 2-ci mərtəbəsi) M1:100

3.9m²; V=5649.0m³

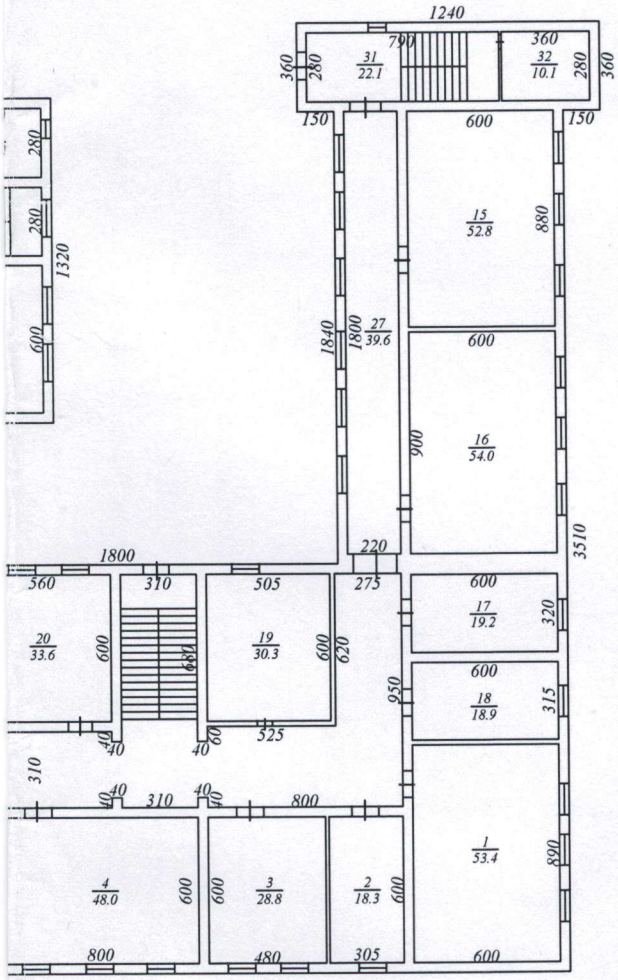


Təsnifat


S/N	OTAQLARIN TƏYİNATI	SAHƏLƏR (m²)		
		ƏSAS	KÖMƏK	DİGƏR
1	Kitabxana	53.4	-	-
2-22	Sinif otağı	818.2	-	-
23-27	Dəhliz	-	381.8	-
28	Hərbi otağı	-	15.6	-
29-31	Pilləkan qəfəsi	-	61.0	-
32-35	Sanitar qovşağı	-	36.4	-
	Cəmi: 1366.4 m²	**871.6**	**494.8**	**####**

Azərbaycan Respublikası
Əmlak Məsələləri Dövlət Komitəsinin yanında
Daşınmaz Əmlakın Dövlət Reyestri Xidmətinin
1 saylı Bakı Ərazi İdarəsi
Daxilolma № 04/6688
« 11 » 09 20 19 il

"A" Tikilisinin planı (4 mərtəbəli bin
h=3.20m; H=3.50m; $S_{t.a.}$=16

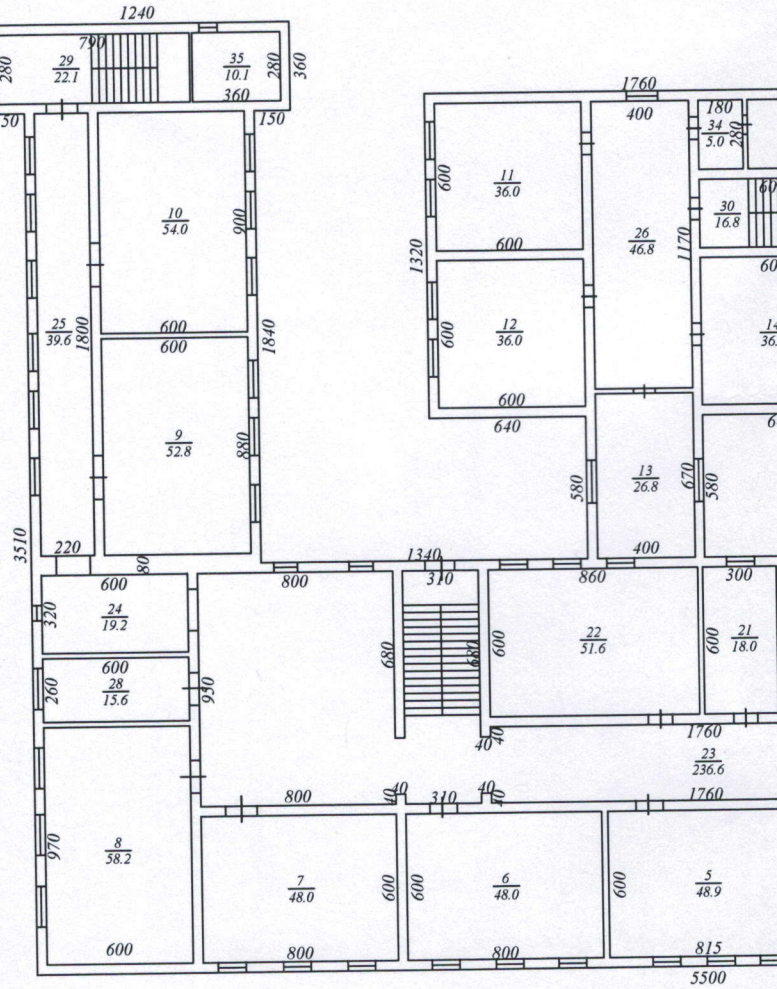

ın 3-cü mərtəbəsi) M1:100
3.9m²; V=5649.0m³

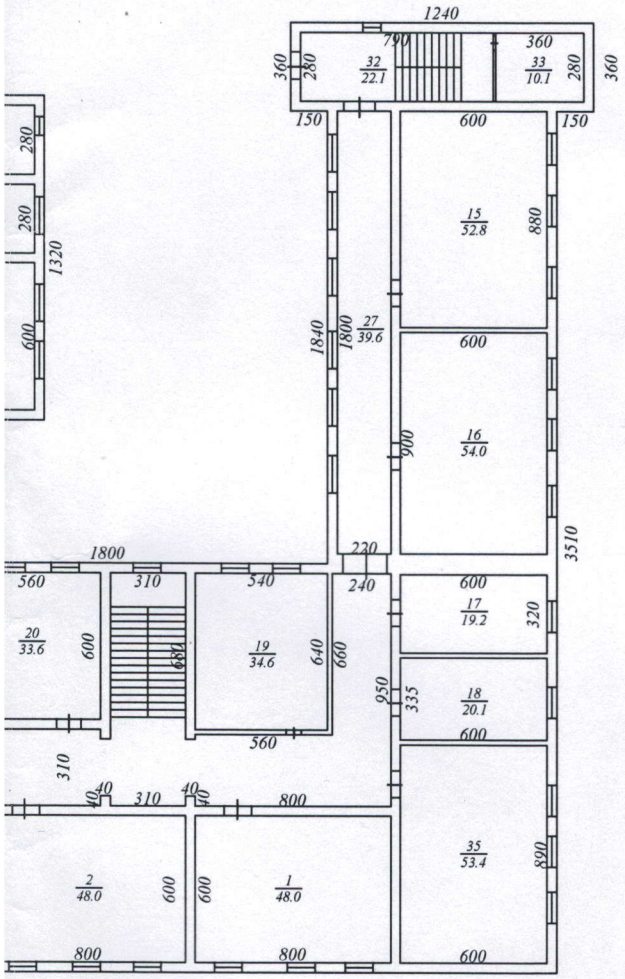


Təsnifat

S/N	OTAQLARIN TƏYİNATI	SAHƏLƏR (m²)		
		ƏSAS	KÖMƏK	DİGƏR
1-20	Sinif otağı	771.2	-	-
21-23	Otaq	69.6	-	-
24-28	Dəhliz	-	377.4	-
29	Labaratoriya	15.0	-	-
30-32	Pilləkan qəfəsi	-	61.0	-
33-34	Sanitar qovşağı	-	20.2	-
35	Muzey	53.4	-	-
	Cəmi: 1367.8 m²	**909.2**	**458.6**	**####**

Azərbaycan Respublikası
Əmlak Məsələləri Dövlət Komitəsinin yanında
Daşınmaz Əmlakın Dövlət Reyestri Xidmətinin
1 saylı Bakı Ərazi İdarəsi
Daxilolma № 04/6688
« 11 » 09 2019-cu il


"A" Tikilisinin planı (4 mərtəbəli bin

h=3.20m; H=3.50m; $S_{t.a.}$=16

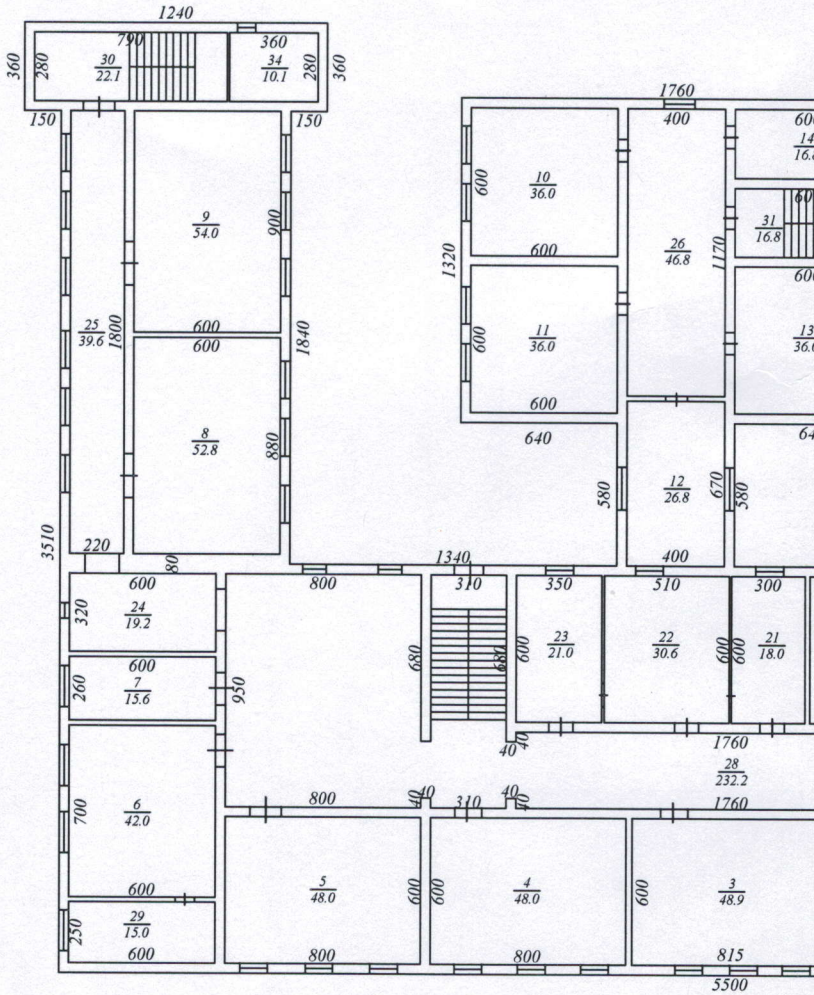

ın 4-cü mərtəbəsi) M1:100

3.9m²; V=5649.0m³

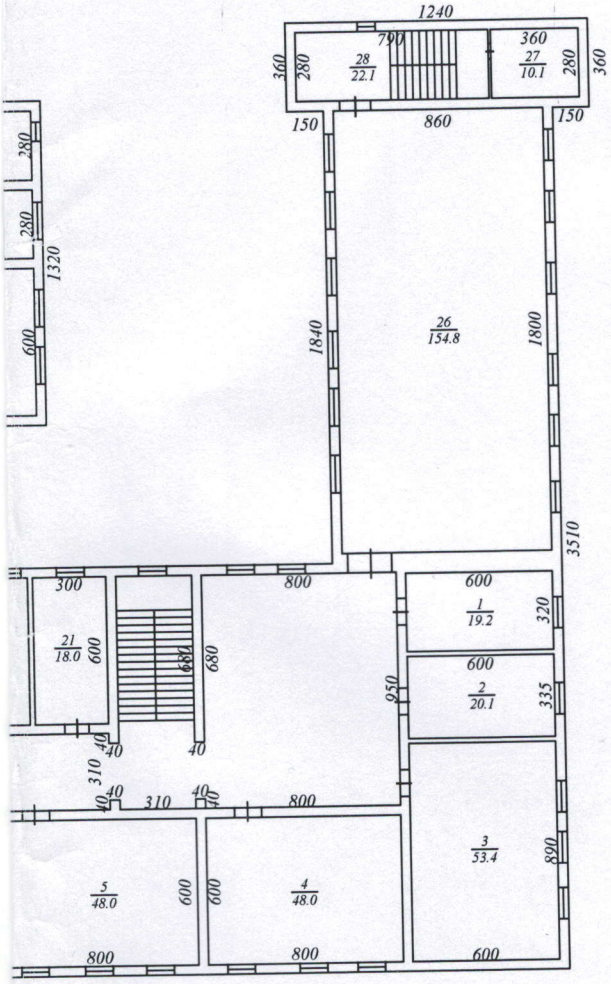


Təsnifat

S/N	OTAQLARIN TƏYİNATI	SAHƏLƏR (m²)		
		ƏSAS	KÖMƏK	DİGƏR
1-21	Sinif otağı	789.2	-	-
22-25	Dəhliz	-	336.6	-
26	Zal	154.8	-	-
27;31	Sanitar qovşağı	-	20.2	-
28-30	Pilləkan qəfəsi	-	61.0	-
32	Otaq	15.6	-	-
Cəmi: 1377.4 m²		**959.6**	**417.8**	**####**

Azərbaycan Respublikası
Əmlak Məsələləri Dövlət Komitəsinin yanında
Daşınmaz Əmlakın Dövlət Reyestri Xidmətinin
1 saylı Bakı Ərazi İdarəsi

Daxilolma № 04/6688
« 11 » 09 20 19 il

"A" Tikilisinin planı (4 mərtəbəli bina
h=3.20m; H=3.50m; $S_{t.a.}$=161

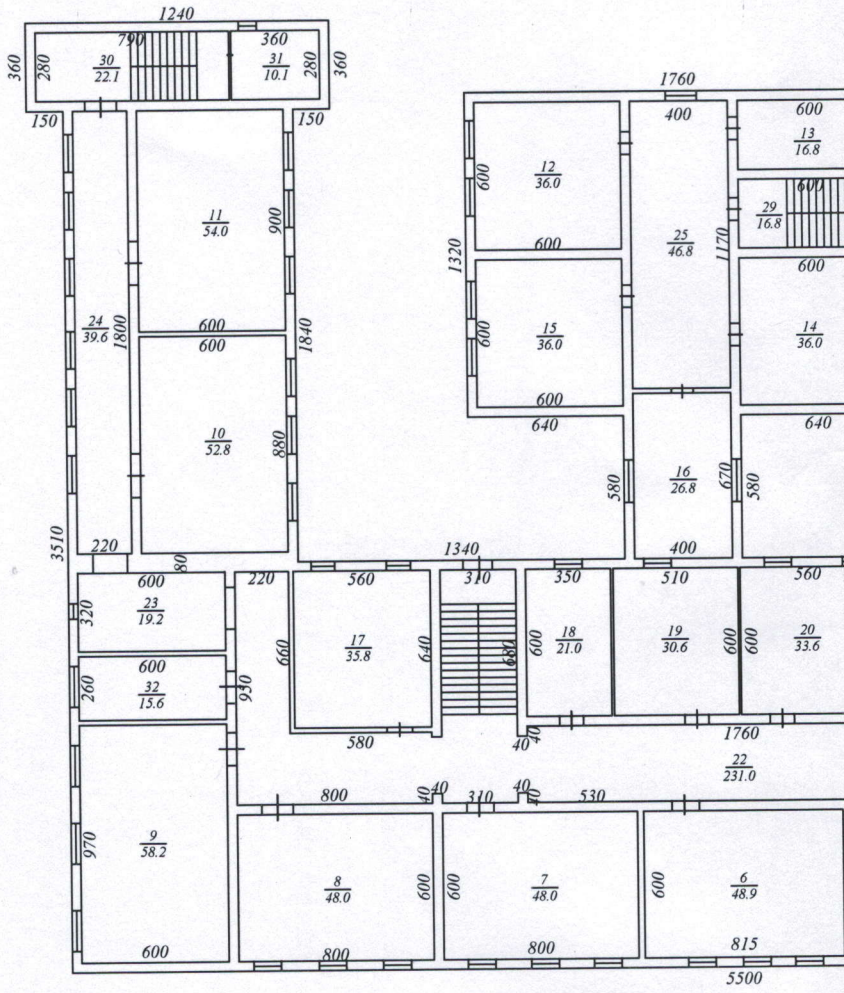

2. *Əsas, köməkçi tikili və qurğuların təyinatı və texniki göstəriciləri*

Liter	Tikililərin və qurğuların təyinatı	Tikildiyi il	Mərtəbəlilik	Otaqların sayı	Tikilialtı sahə, kv.m		Hündürlüyü, H.m.	Həcmi, kub.m.	Daxili hündürlüyü, h.m.	Faydalı sahə kv.m.					Köhnəlmə faizi	Pasportun tərtib edildiyi tarixə obyektin dəyəri (manatla)
					əsas	digər				Ümumi sahə	Əsas sahə	Köməkçi sahə	Digər sahələr	Xidməti sahə		
A	Məktəb binası		4	-	2100.5	44.9	15.3	28725.0	14.1	7042.7	4244.5	2798.2	50.6	-		
I	Su anbarı		-	-	-	54.0	-	-	-	-	-	-	-	-		
II	Nasosxana		-	-	-	41.0	-	-	-	-	-	-	-	-		
III	Daş hasar L=236.2 b=0.2		-	-	-	47.2	-	-	-	-	-	-	-	-		
IV	Dəmir barmaqlı darvaza(2ədəd)		-	-	-	-	-	-	-	-	-	-	-	-		

Azərbaycan Respublikası
Əmlak Məsələləri Dövlət Komitəsinin yanında
Daşınmaz Əmlakın Dövlət Reyestri Xidmətinin
1 saylı Bakı Ərazi İdarəsi
Daxiloluma № 04/6688
«11» 09 2019

3.Torpaq sahəsinin planı

M:1

Su təchizatı	Qaz təchizatı	Elektrik təchizatı	Kanalizasiya təchizatı	İsti su təchizatı	Suqızdırma sistemi	Digər abadlıq elementləri

Şərti istinad planı

	X	Y
Obyektin koordinatları	401855.2885	4476768.3617
	401834.2416	4476793.2572
	401839.6373	4476809.7460
	401846.2572	4476833.6128
	401916.2146	4476811.9414
	401915.5054	4476808.6848
	401917.2654	4476808.2948
	401916.2954	4476804.0048
	401917.1254	4476802.1948
	401937.0169	4476796.4660
	401937.5606	4476798.1592
	401942.0305	4476796.1516
	401937.8854	4476789.4748

Ərazi idarəsinin adı: 1 saylı Bakı Ərazi İdarəsi

	Soyadı,adı,atasının adı	İmza	Tarix	Obyektin ünvanı
Tərtib etdi	M.Həsənli		21.08.19	Bakı şəhəri, Binəqədi rayonu, M.Ə.Rəsulzadə qəsəbəsi, Azadlıq prospekti, 193
Yoxladı	O.Kərimov		21.08.19	

4.Torpaq sahəsinin təsnifatı

torpaq ayırma sənədləri üzrə	faktiki istifadə	o cümlədən						
		əsas tikili altında	digər tikili və qurğular altında	asfalt örtüklü	beton örtüklü	yaşıllıq örtüklü	sərbəst (örtüksüz) torpaq	digər
-	0.56133	0.21005	0.01875	-	-	-	0.33257	-

Azərbaycan Respublikası
Əmlak Məsələləri Dövlət Komitəsinin sənədlərin
Daşınmaz Əmlak üzrə Dövlət Reyestri Xidmətinin
Bakı Ərazi İdarəsi
Daxiloima № 04/6682
«11» 09 2019

5.Mərtəbələr üzrə plan

M:1

	Ərazi idarəsinin adı: 1 saylı Bakı Ərazi İdarəsi				
		Soyadı,adı,atasının adı	İmza	Tarix	Obyektin ünvanı
	Tərtib etdi	M.Həsənli		21.08.19	Bakı şəhəri, Binəqədi rayonu, M.Ə.Rəsulzadə qəsəbəsi, Azadlıq prospekti, 193
	Yoxladı	O.Kərimov		21.08.19	

Azərbaycan Respublikası
Əmlak Məsələləri Dövlət Komitəsinin yanında
Daşınmaz Əmlakın Dövlət Reyestri Xidmətinin
1 saylı Bakı Ərazi İdarəsi

Daxilolma № 04/6688

« 11 » 09 2019 il

6.Obyektin mərtəbələr üzrə planının eksplikasiyası

Liter	Mərtəbə	Plan üzrə otaqların nömrəsi	Otaqların təyinatı	Sahəsi kv.m.				Daxili hündürlüyü, h.m.	Qeyd
				ümumi sahə (kv. m.)	o, cümlədən				
					əsas	köməkçi	digər sahələr		
A	zirzəmi	1-23	Zirzəmi	828.0	828.0	-	-	2.2	
A	zirzəmi	24-26	Dəhliz	251.1	-	251.1	-	2.2	
A	zirzəmi	27	Açıq pilləkən	-	-	-	5.7	-	
A	zirzəmi	28.29	Giriş	65.0	-	65.0	-	2.2	
A	1	1,6,7,10,11	Sinif otağı	234.8	234.8	-	-	3.3	
A	1	2.3,4,29,34	Dəhliz	367.0	-	367.0	-	3.3	
A	1	5,28,42	Pilləkən qəfəsi	81.8	-	81.8	-	3.3	
A	1	8.9,12	İş otağı	40.5	40.5	-	-	3.3	
A	1	13,14,30,50	İş otağı	60.6	60.6	-	-	3.3	
A	1	15	Drektor otağı	30.0	30.0	-	-	3.3	
A	1	16,24-27	Sinif otağı	133.2	133.2	-	-	3.3	
A	1	17	Tibb otağı	18.3	-	18.3	-	3.3	
A	1	18,19,39.51	Anbar	60.6	-	60.6	-	3.3	
A	1	20,21,31,32	Sanitar qovşağı	20.4	-	20.4	-	3.3	
A	1	22	Yeməkxana	37.8	-	37.8	-	3.3	
A	1	23	Mətbəx	19.2	-	19.2	-	3.3	
A	1	33,36,41,45	Sinif otağı	141.0	141.0	-	-	3.3	
A	1	35,40,47,52	Dəhliz	156.5	-	156.5	-	3.3	
A	1	37,38,43,44	Sanitar qovşağı	31.4	-	31.4	-	3.3	
A	1	46	Sinif otağı	36.0	36.0	-	-	3.3	
A	1	48,49	S/G otağı	38.8	-	38.8	-	3.3	
A	1	53	İdman zalı	279.1	-	279.1	-	6.0	
A	1	54	Açıq pilləkən	-	-	-	44.9	-	
A	2	1	Kitabxana	53.4	53.4	-	-	3.2	
A	2	2-22	Sinif otağı	818.2	818.2	-	-	3.2	
A	2	23-27	Dəhliz	381.8	-	381.8	-	3.2	
A	2	28	Hərbi otağı	15.6	-	15.6	-	3.2	
A	2	29-31	Pilləkən qəfəsi	61.0	-	61.0	-	3.2	
A	2	32-35	Sanitar qovşağı	36.4	-	36.4	-	3.2	
A	3	1-20	Sinif otağı	771.2	771.2	-	-	3.2	
A	3	21-23	Otaq	69.6	69.6	-	-	3.2	
A	3	24-28	Dəhliz	377.4	-	377.4	-	3.2	
A	3	29	Laboratoriya	15.0	15.0	-	-	3.2	
A	3	30-32	Pilləkən qəfəsi	61.0	-	61.0	-	3.2	
A	3	33-34	Sanitar qovşağı	20.2	-	20.2	-	3.2	
A	3	35	Muzey	53.4	53.4	-	-	3.2	
A	4	1-21	Sinif otağı	789.2	789.2	-	-	3.2	
A	4	22-25	Dəhliz	336.6	-	336.6	-	3.2	
A	4	26	Zal	154.8	154.8	-	-	3.2	
A	4	27,31	Sanitar qovşağı	20.2	-	20.2	-	3.2	
A	4	28-30	Pilləkən qəfəsi	61.0	-	61.0	-	3.2	
A	4	32	Otaq	15.6	15.6	-	-	3.2	
			Cəmi	**7042.7**	**4244.5**	**2798.2**	**50.6**		

Azərbaycan Respublikası
Əmlak Məsələləri Dövlət Komitəsinin yanında
Daşınmaz Əmlakın Dövlət Reyestri Xidmətinin
I saylı Bakı Ərazi İdarəsi
Daxilolma № 04/6588
12 09 19 il

7.Əsas tikililərin texniki təsviri və vəziyyəti

Sıra N.	Konstruktiv elementlər			
	adı	xarakteristikası (materialı,konstruksiyası və s.)	texniki vəziyyət	köhnəlmə faizi
1	Bünövrə	beton	-	
2	Daxili divar	m/daşı	-	
3	Xarici divar	m/daşı	-	
4	Su təchizatı	var	-	
5	Elektrik təchizatı	var	-	
6	Kanalizasiya	var	-	

Azərbaycan Respublikası
Əmlak Məsələləri Dövlət Komitəsinin yanında
Daşınmaz Əmlakın Dövlət Reyestri Xidmətinin
1 saylı Bakı Ərazi İdarəsi
Daxilolma № 04/6688
« 11 » 09 20 19 il

8. Həyət tikililəri və qurğuların texniki təsviri və vəziyyəti

Həyət tikililəri

Liter	Tikintinin adı	Texniki təsviri				
		Divarlar	Döşəmələr	Dam	Sanitariya texnikası	Ümumi fiziki köhnəlmə

Quyular

Liter	Quyuların dərinliyi	Daxili üfüqi kəsiyin sahəsi	Texniki təsviri və vəziyyəti	Ümumi fiziki köhnəlmə

Hovuzlar

Liter	Xarici üfüqi kəsiyin sahəsi	Daxili tutumu, kub m.	Texniki təsviri və vəziyyəti	Ümumi fiziki köhnəlmə

Hasarlar

Liter	Hasarın materialı	Uzunluğu, m	Orta hündürlüyü, m	Divarların sahəsi, kv,m	Xarakteristikası və texniki vəziyyəti	Ümumi fiziki köhnəlmə

Darvaza və qapılar

Liter	Darvazanın materialı	Qapının materialı	Hündürlüyü və eni	Xarakteristikası və texniki vəziyyəti	Ümumi fiziki köhnəlmə

Digər qurğular

Liter	Adı	Xarakteristikası və texniki vəziyyəti	Ümumi fiziki köhnəlmə

Pasportun tərtib edilməsi üçün təqdim edilmiş sənədlər:
07.08.2019-ci il tarixli, 875 nömrəli Registrdən çıxarış, ;

Şöbə müdiri: C.Orucəliyev

Sektor müdiri N.Qəniyev

Passportu tərtib etdi: Ş.Mirzəyeva

Yoxladı: Q.Kərimov

Azərbaycan Respublikası
Əmlak Məsələləri Dövlət Komitəsinin yanında
Daşınmaz Əmlakın Dövlət Reyestri Xidmətinin
1 saylı Bakı Ərazi İdarəsi
Daxilolma № 04/6688
«11» 09 2019 il